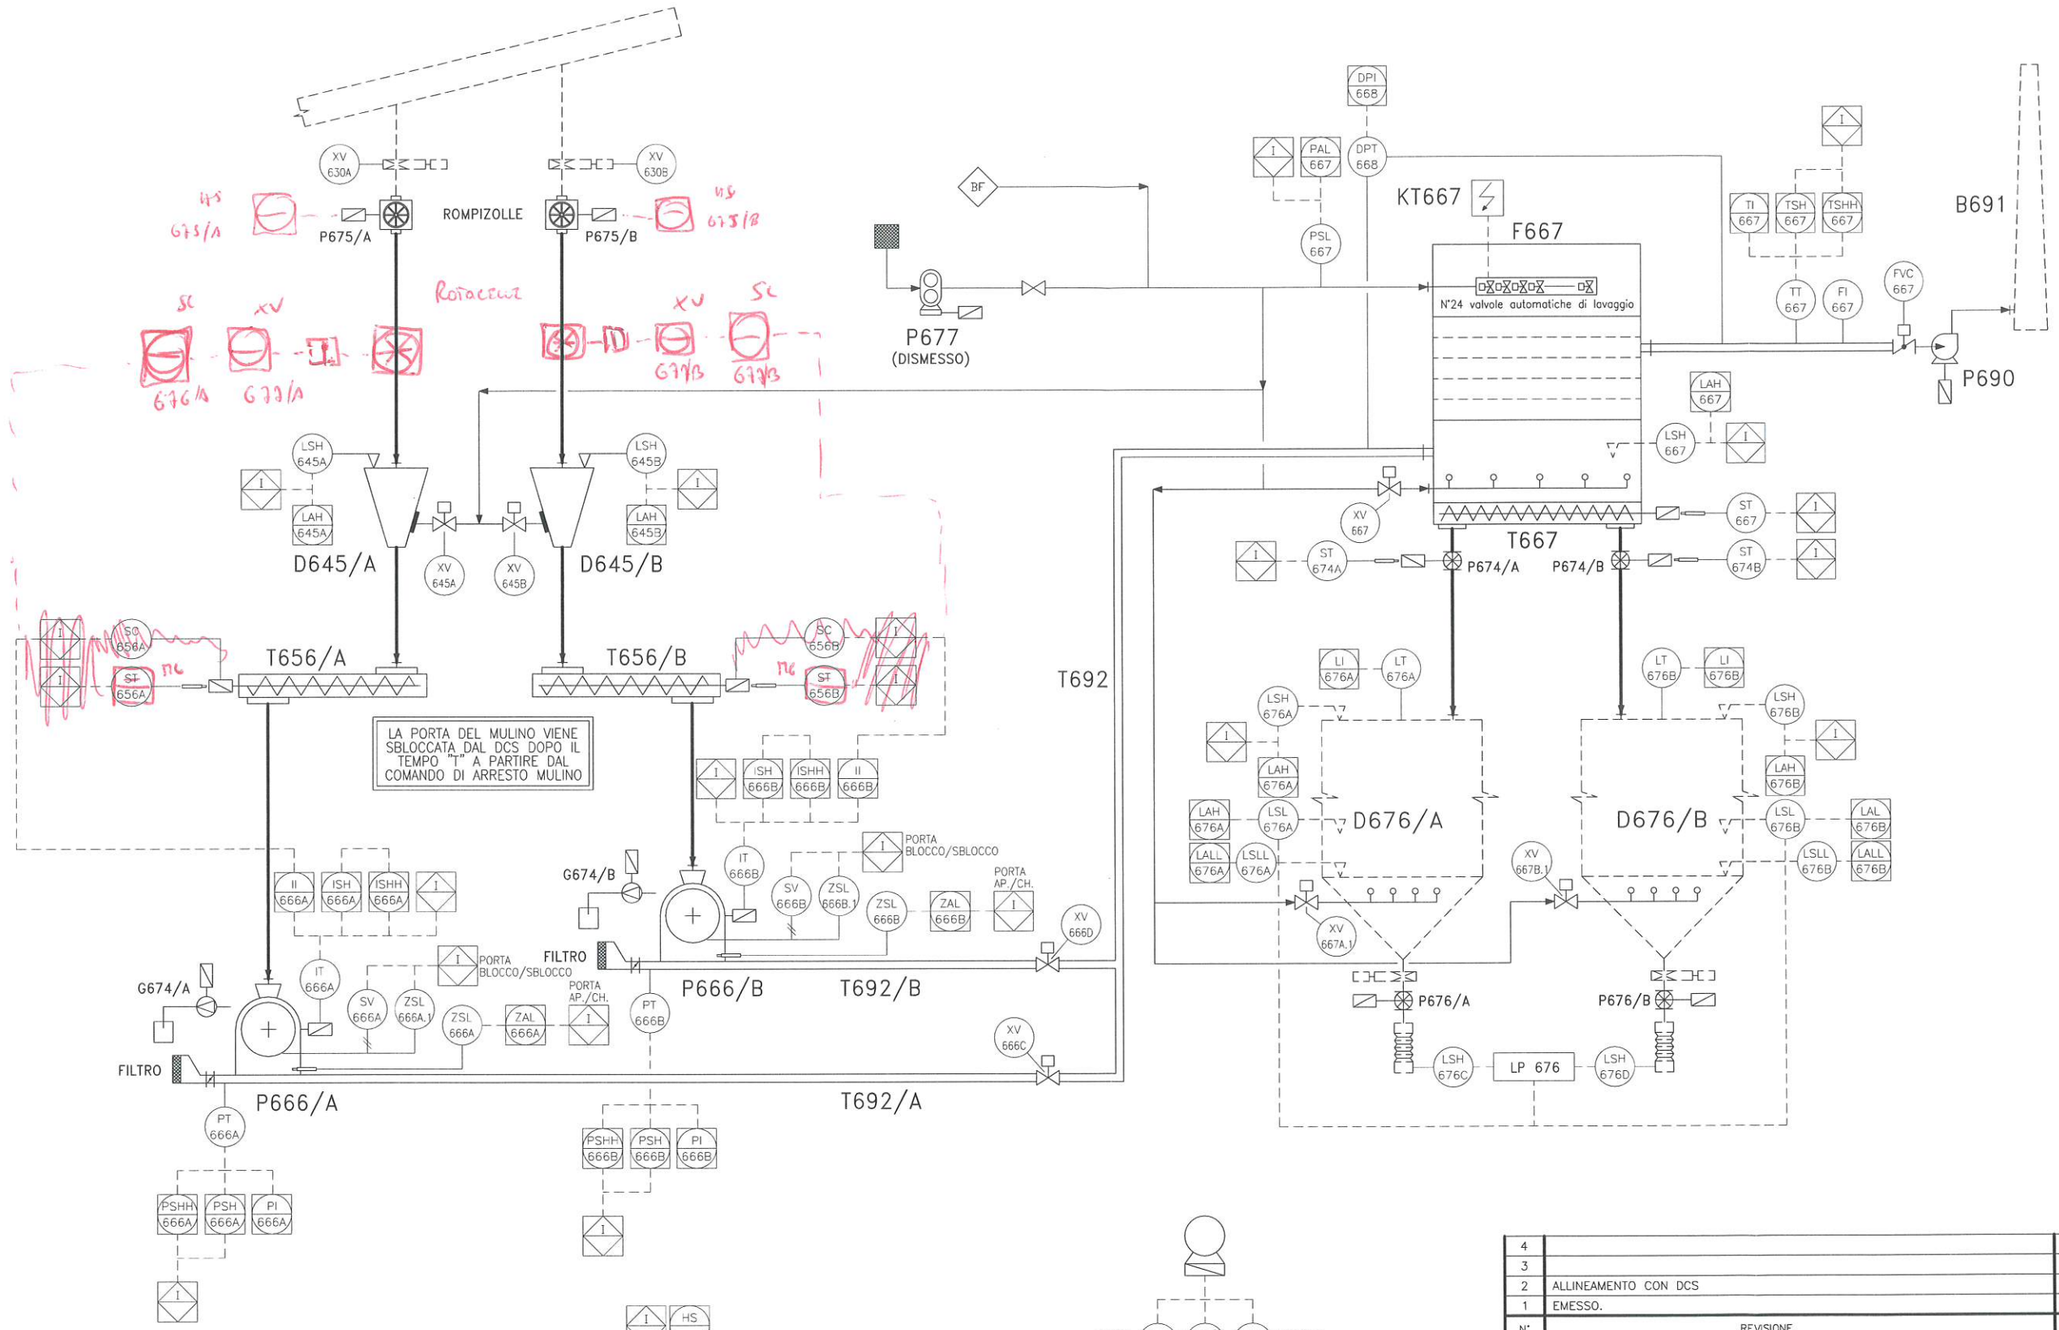

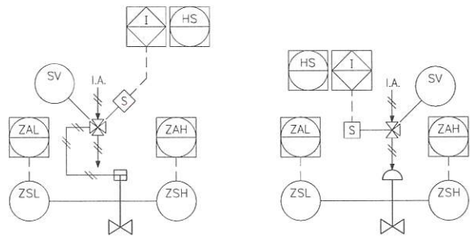

TIPICO PER VALVOLE ON-OFF

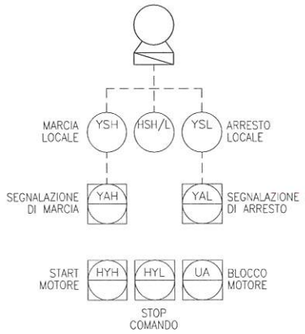

TIPICO PER MOTORI

N°	REVISIONE	DATA	DISEGN.	APPR.
4				
3				
2	ALLINEAMENTO CON DCS	10.12.18	F.B.-PS	
1	EMESSO.	12.03.15	V.P.	

Alkeemia — a FluoroMidGroup Company

Il presente disegno e' di proprieta' della **ALKEEMIA** SpA
Senza autorizzazione scritta della stessa non potra' essere comunque utilizzato per la costruzione dell'oggetto rappresentato, ne venire comunicato a terzi o riprodotto. La societa' proprietaria tutela i propri diritti a rigore di legge.

U.E.	Numero progres.	N°Fgl.
MN	F-2932	001
REV.	REPARTO	C.T.
02	GG-1	Z
U.D.	DATA	S.C.T.
	120315	

TITOLO:

Stab. di Porto Marghera
IMPIANTO MACINAZIONE GESSI
SCHEMA DI MARCIA

VENETA PROGETTI

SCALA:	SOSTITUITO DA:	SOSTITUISCE IL:	DISEGN.	APPROVATO
		(RESIMONT) 00162-001 Rev.07	VENETA PROGETTI	

Formato A2